


Site Section

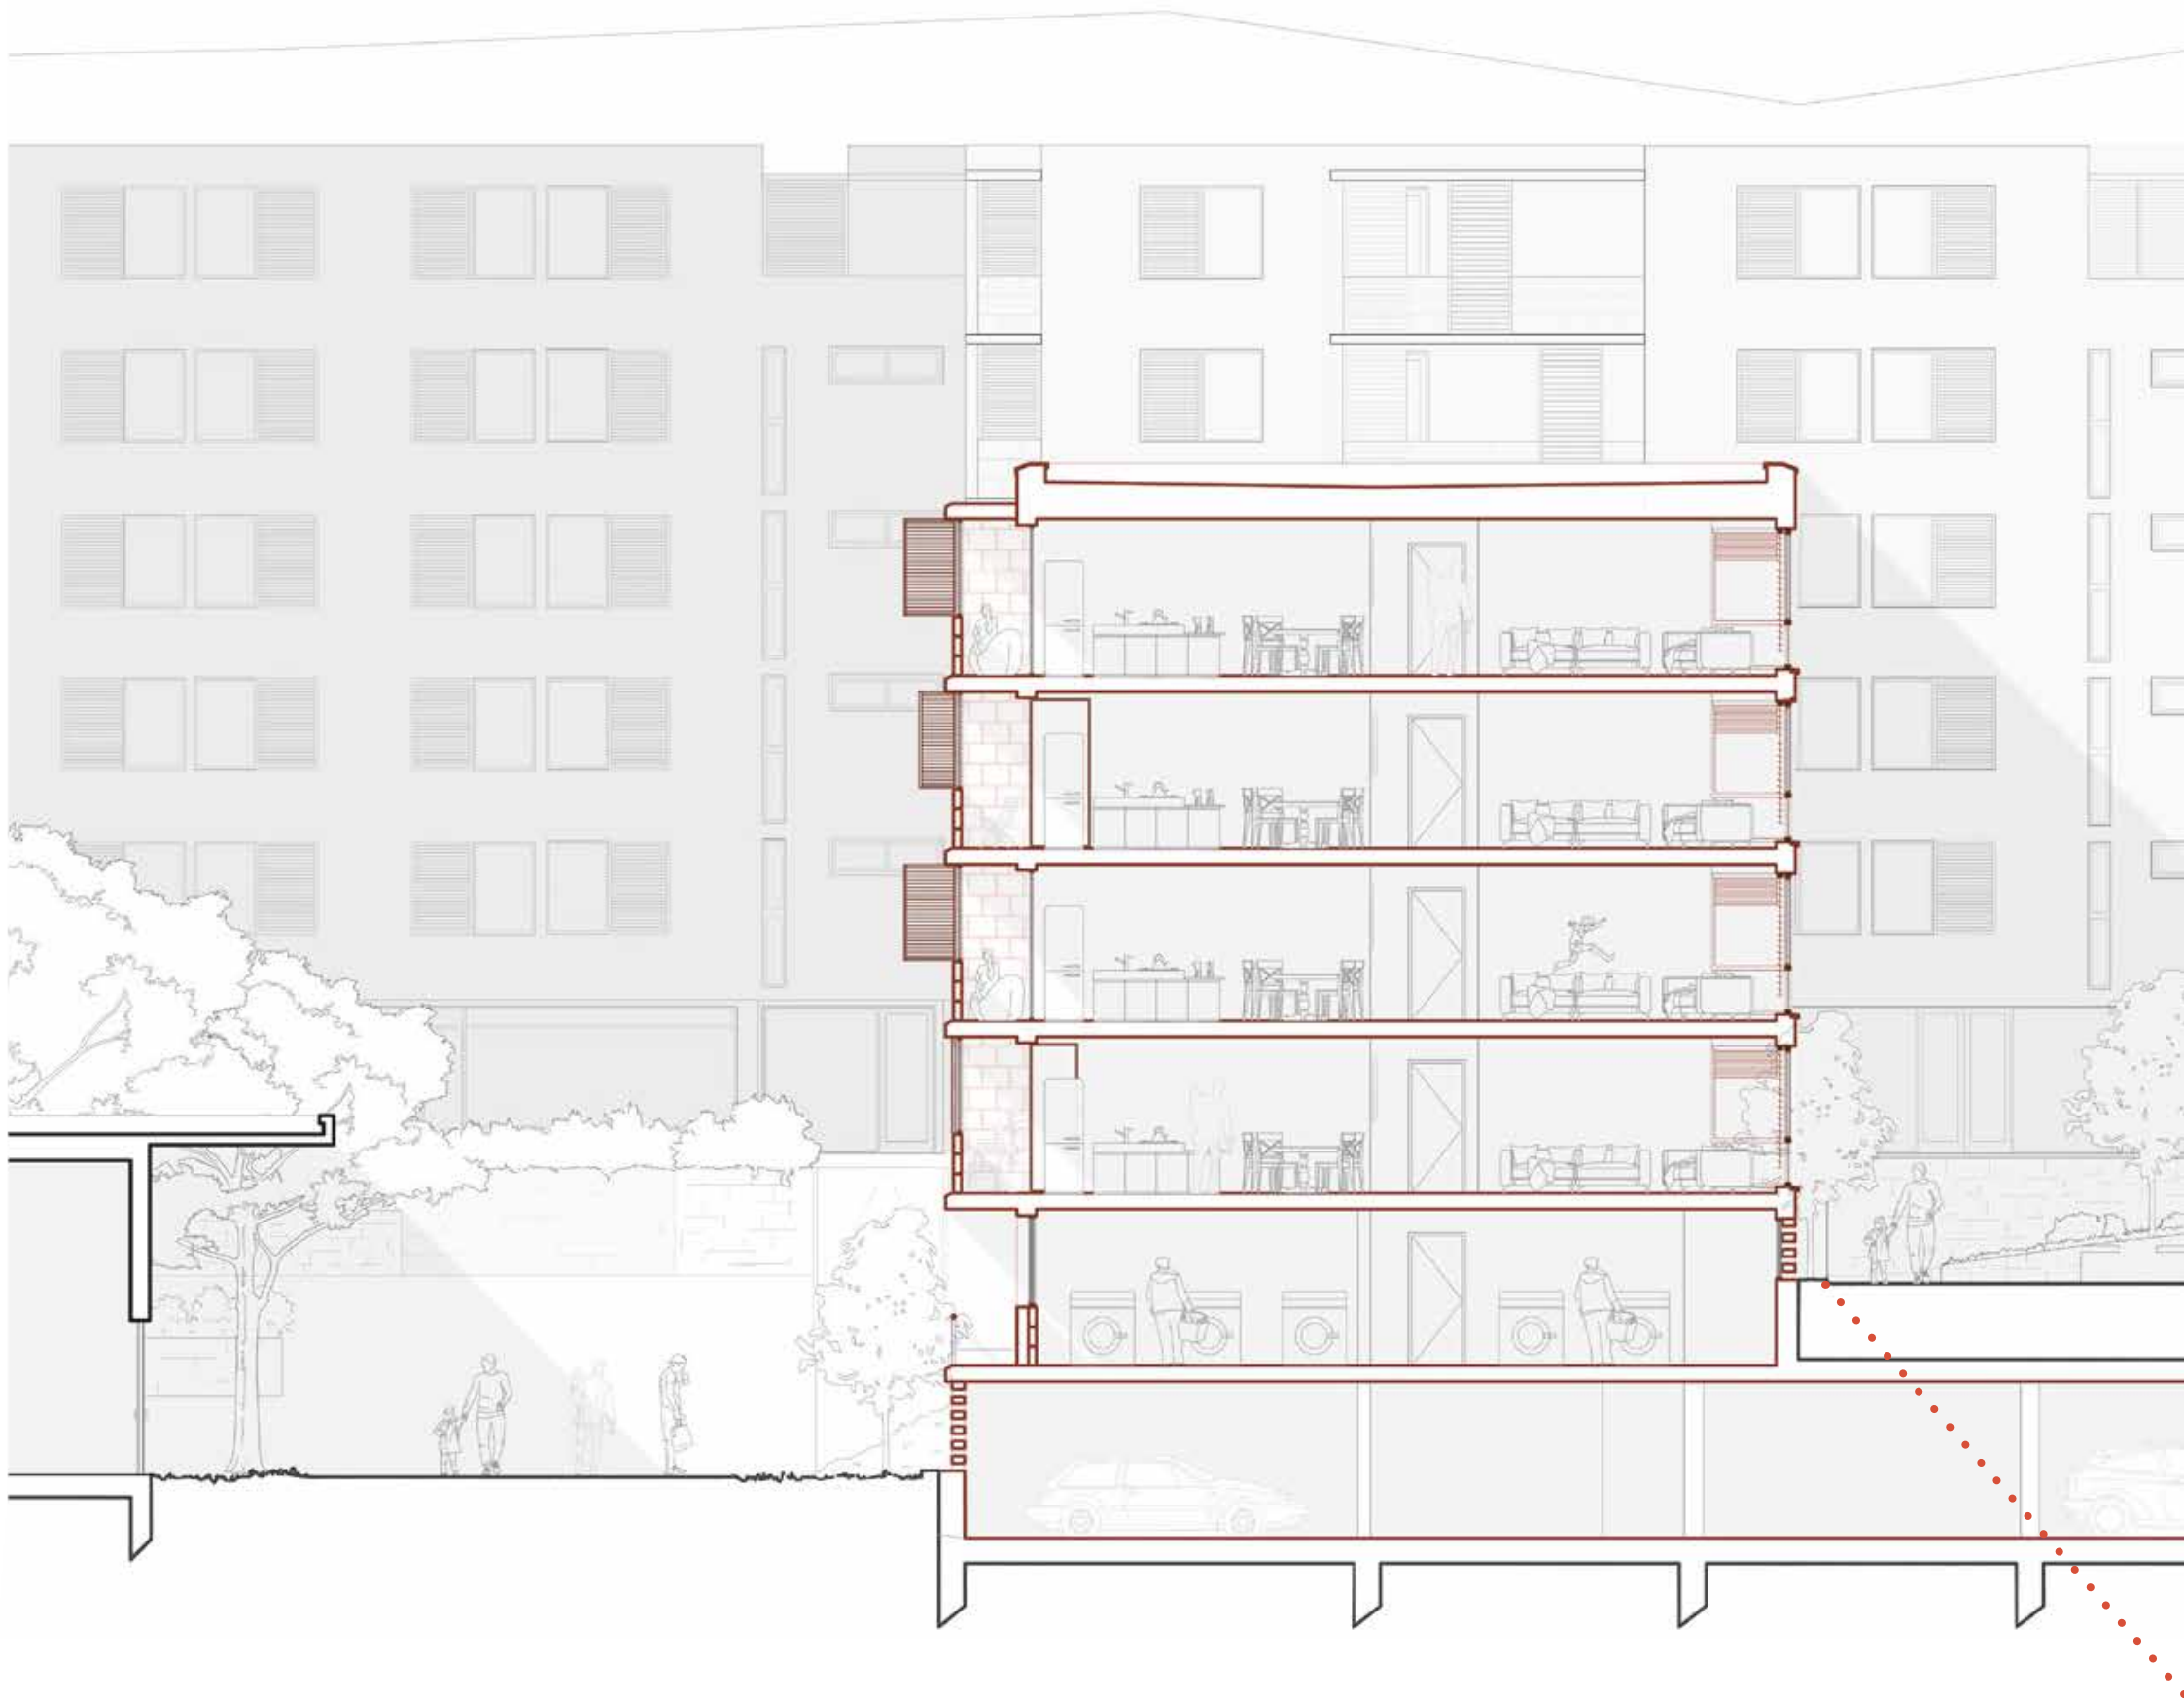

Typical Floor Plan (T6)

