
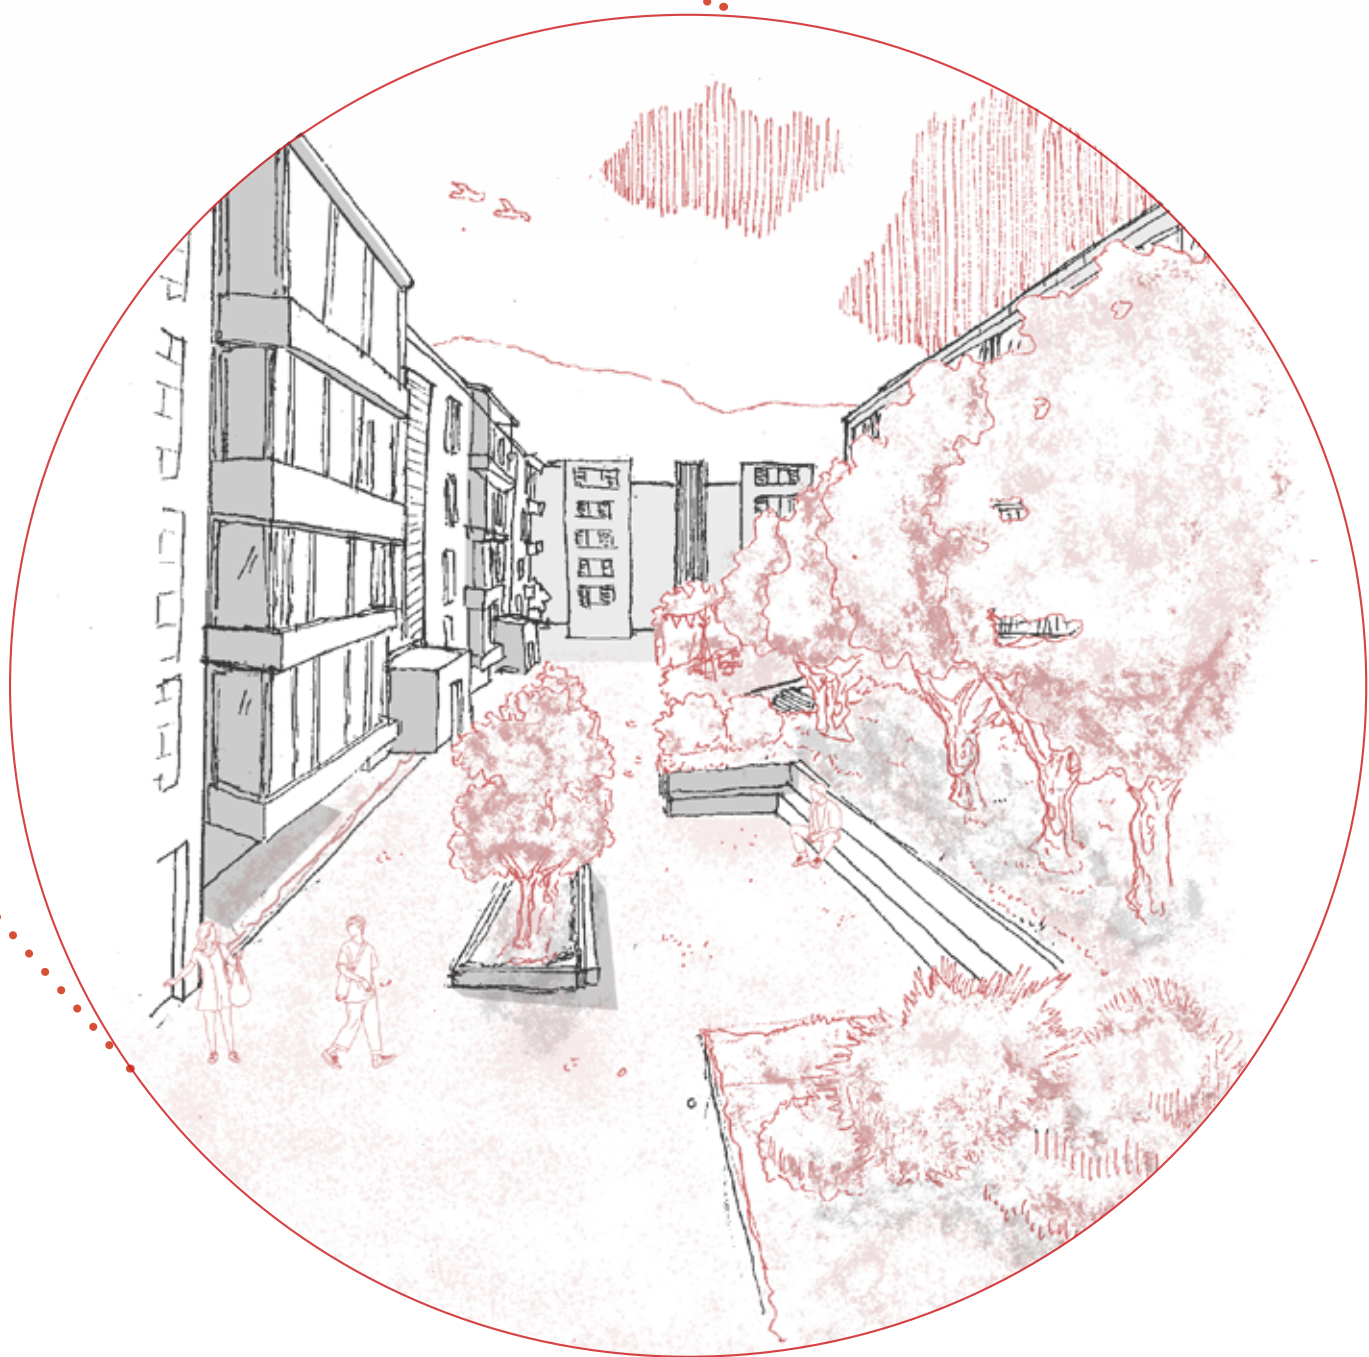
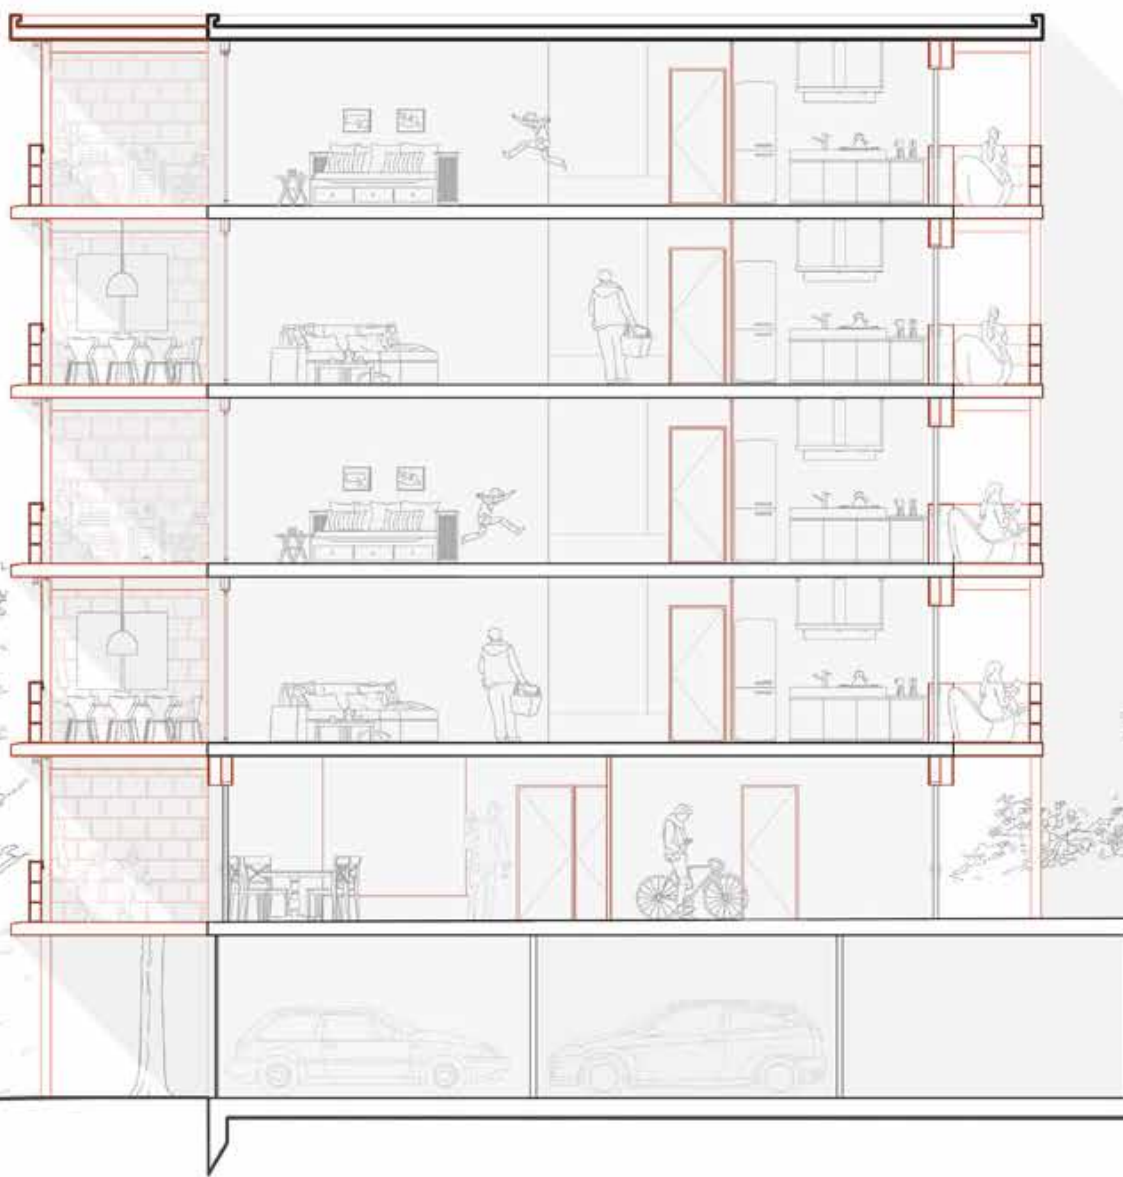


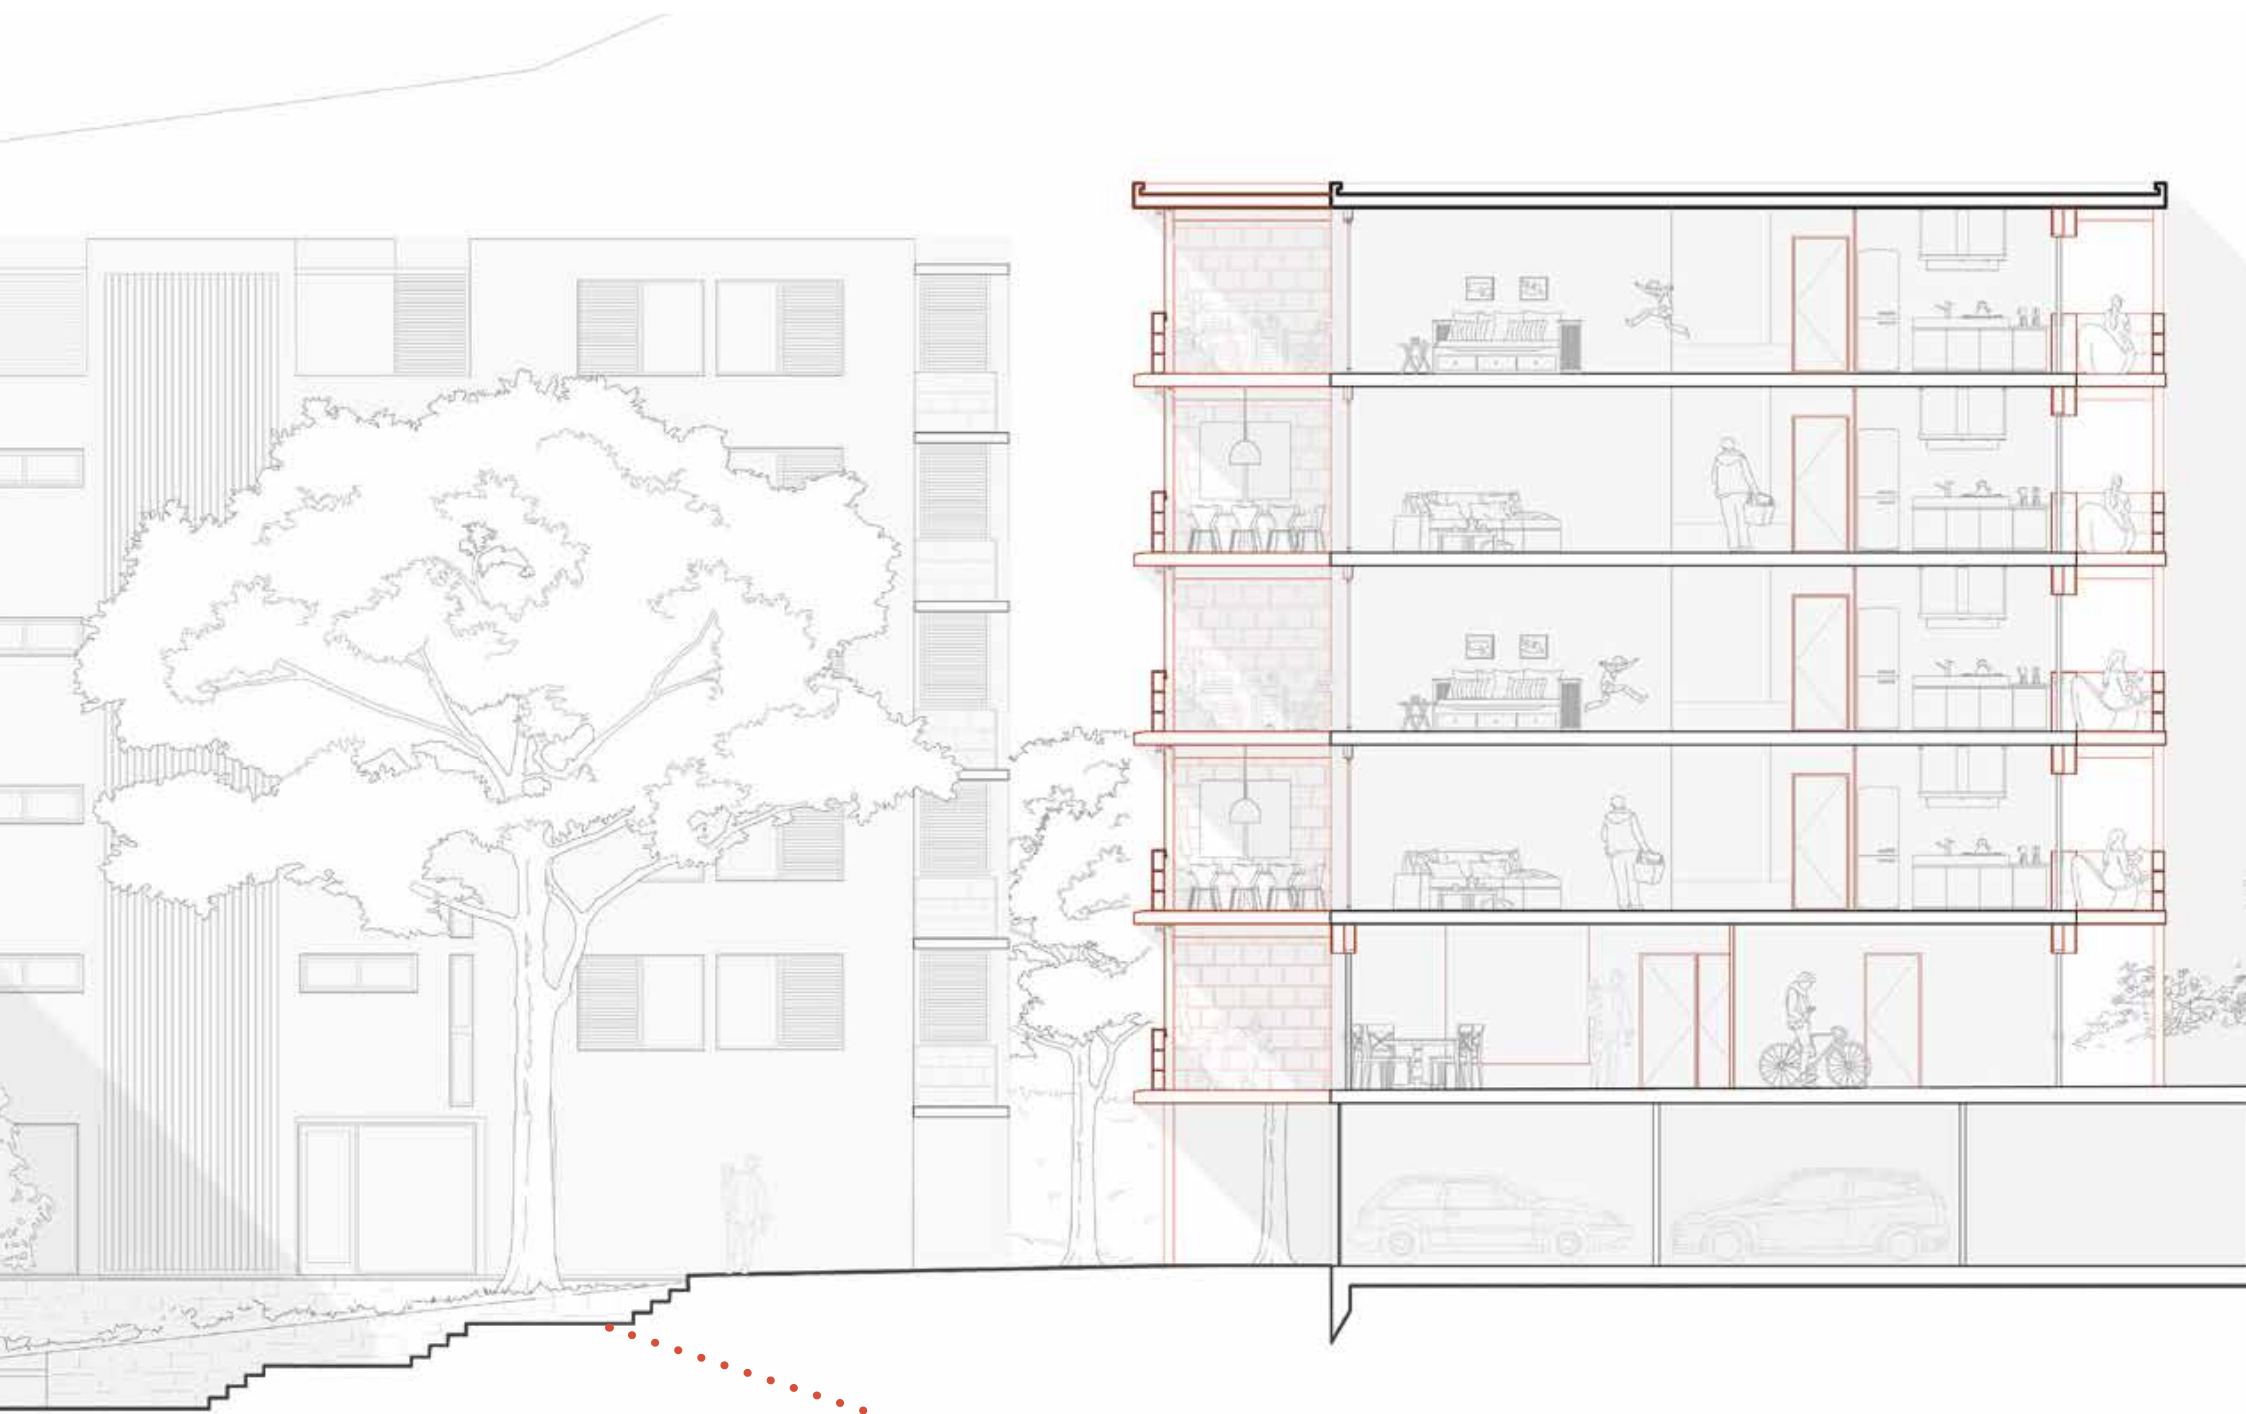

Perspective view of inner courtyard