


Façade View 1:20



Détail façade Nord
1:20

Détail plan
1:20

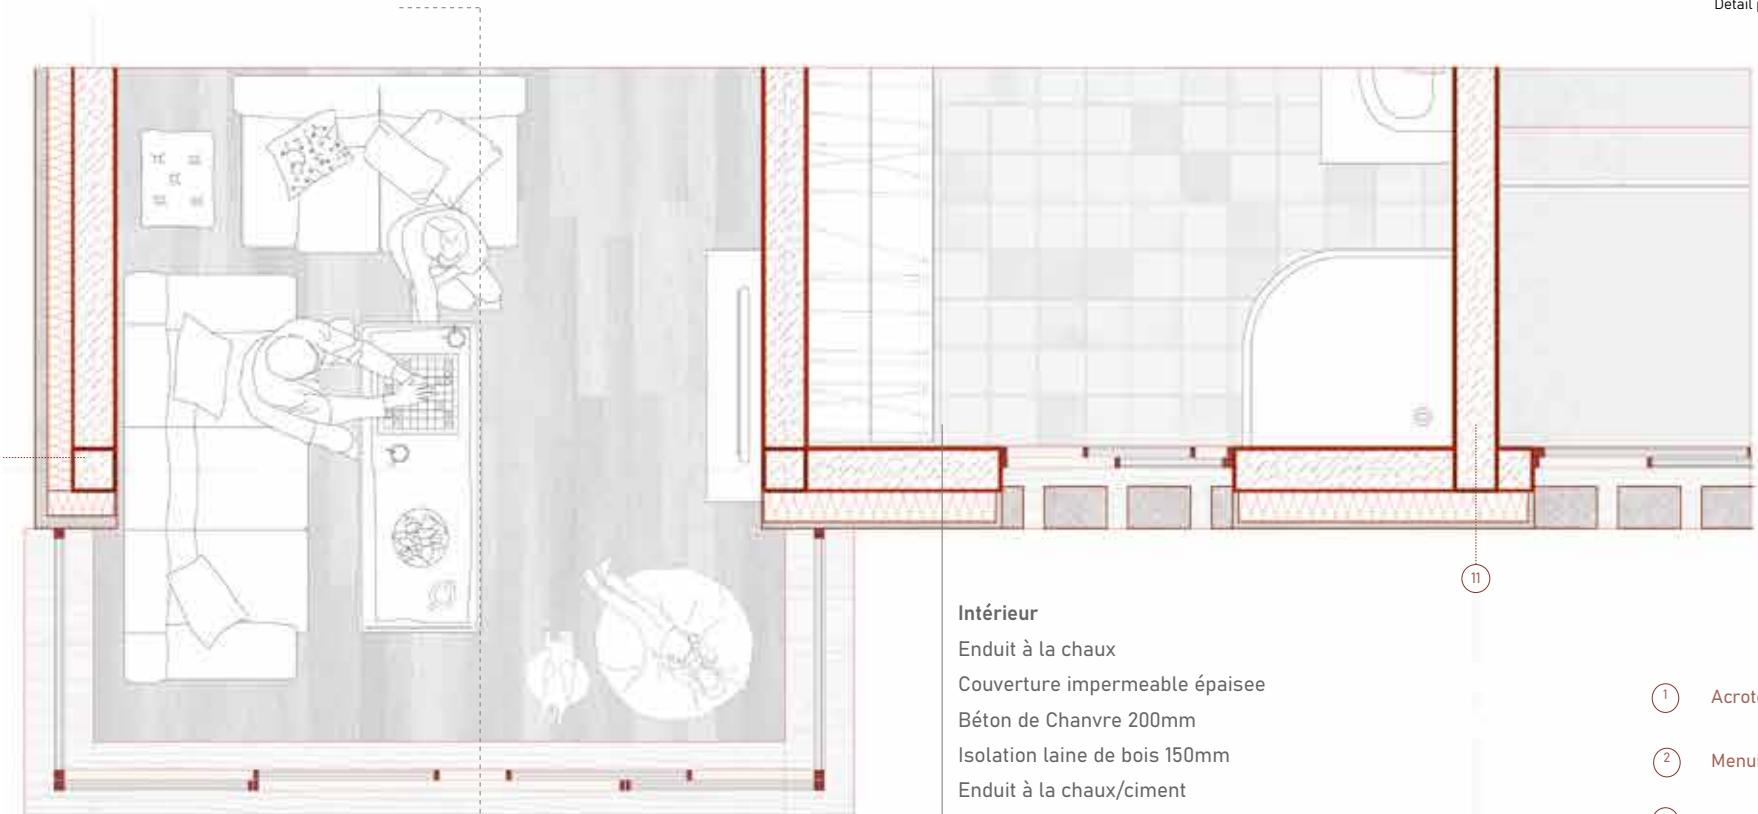

Intérieur
Enduit à la chaux
Couverture impermeable épaisse
Béton de Chanvre 200mm
Isolation laine de bois 150mm
Enduit à la chaux/ciment
Extérieur

- ① Acrotère en zinc
- ② Menuiserie en bois
- ③ Rebord de fenêtre
- ④ Protection solaire- persiennes intérieures en bois
- ⑤ Connecteur de balcon en acier
- ⑥ Poteau béton armé 200x200mm

Plan View 1:20