


Section 1:20

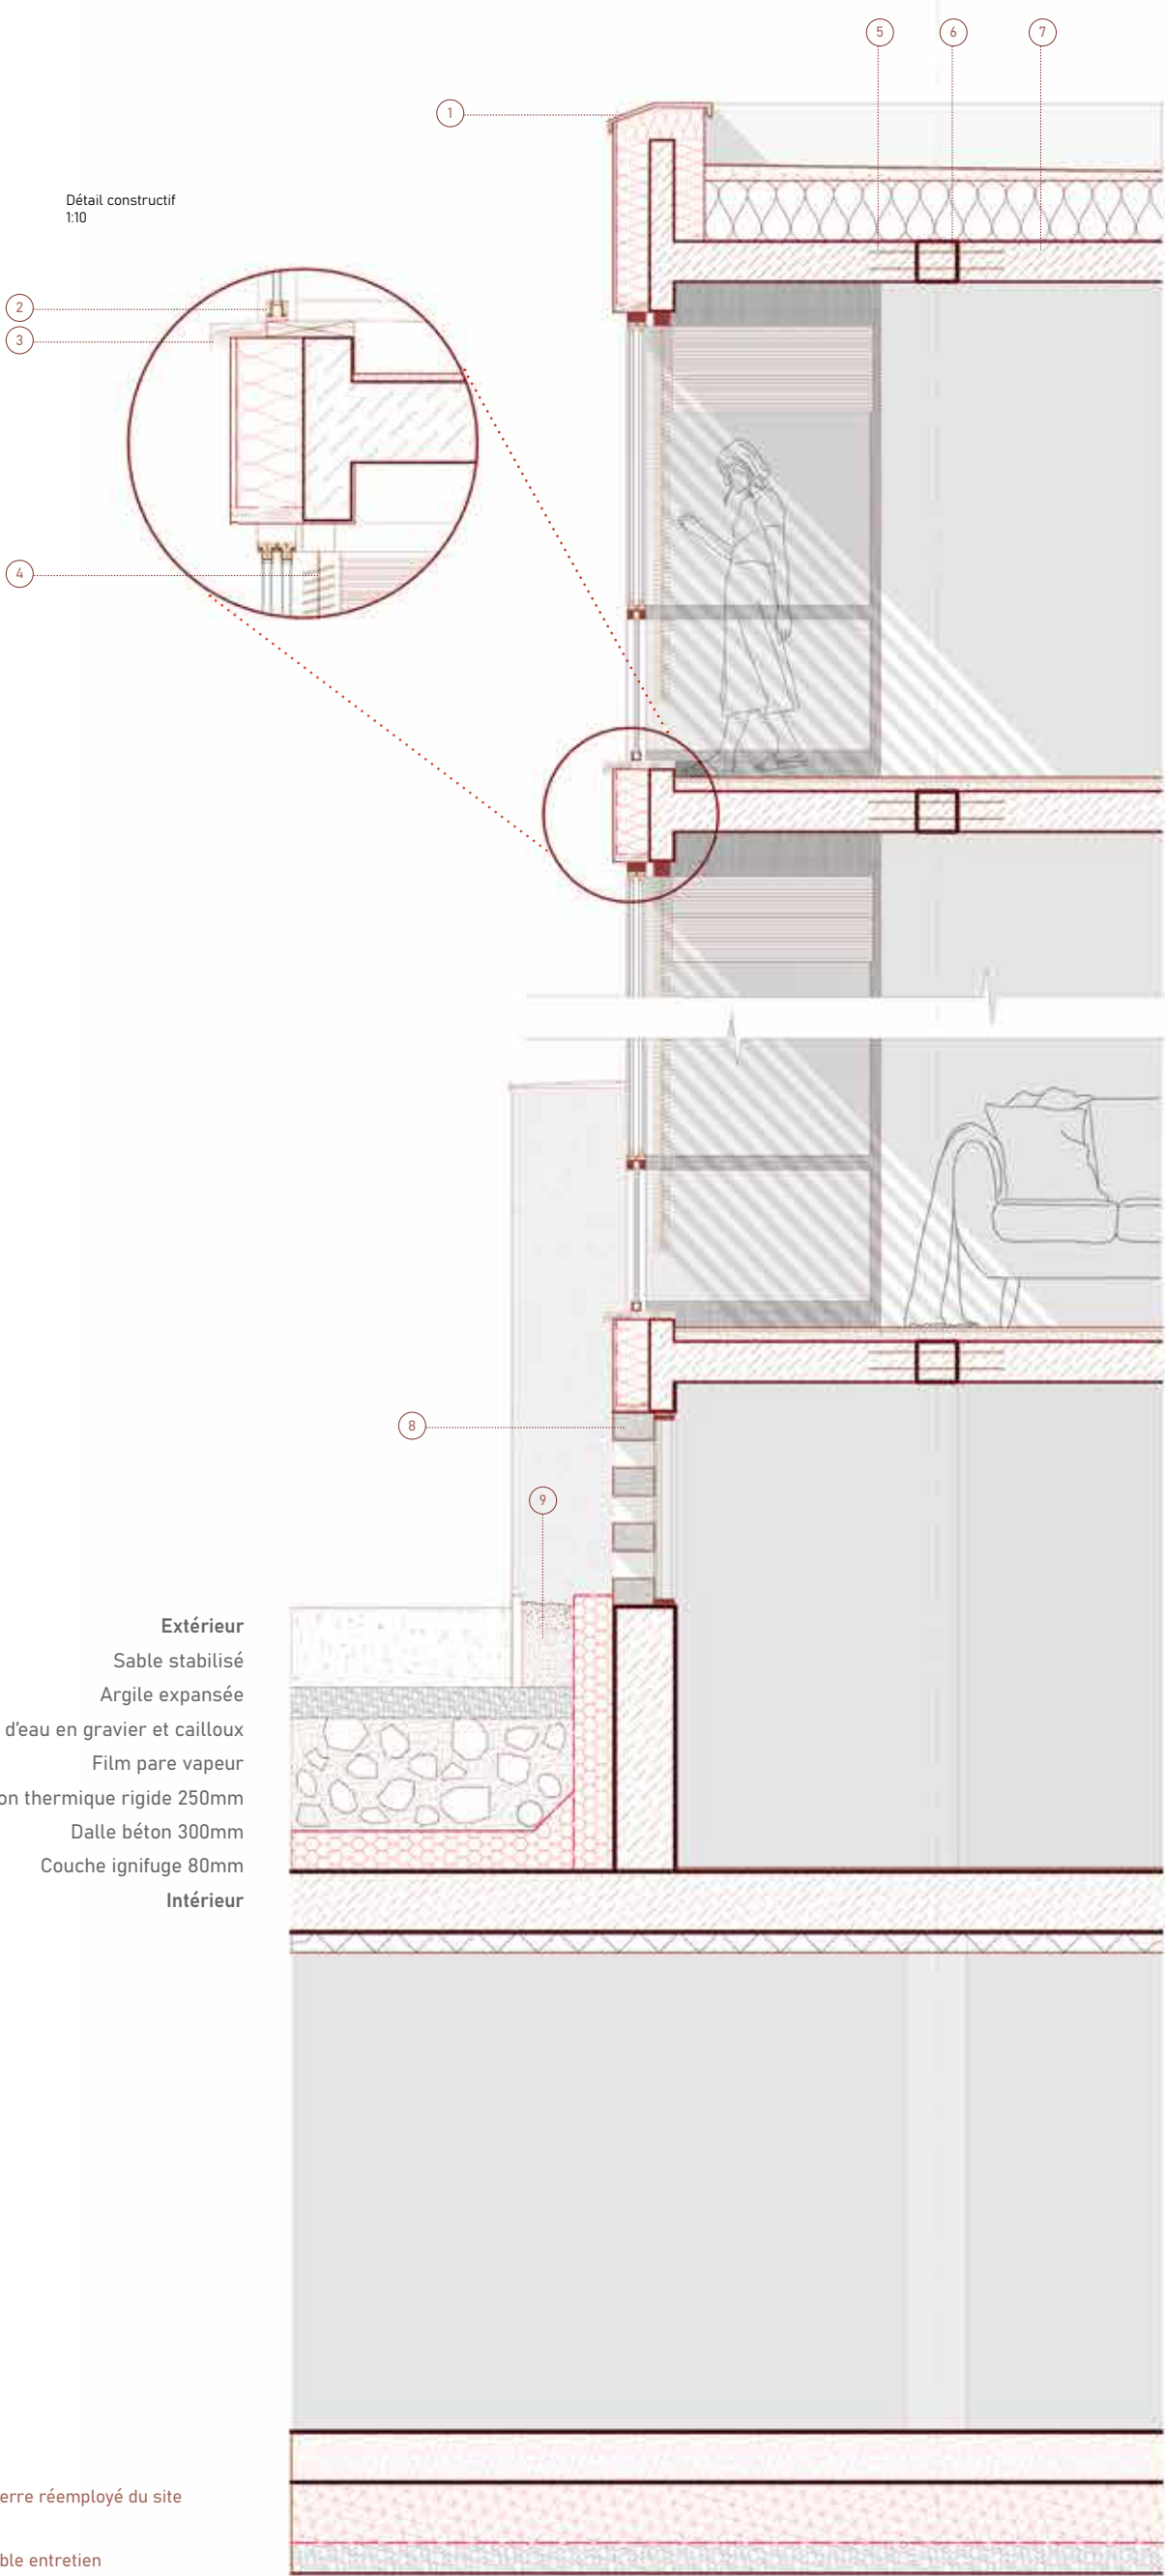

TOITURE

Extérieur
Film Pare pluie
Isolation laine de bois 300mm avec pente intégré
Film pare vapeur
Dalle béton 200mm
Enduit à la chaux
Intérieur

R + 4

Parquet
Chape avec chauffage au sol
Film isolation acoustique
Dalle béton 200mm
Enduit à la chaux

R+1 (demi-niveau)

RDC

Chape avec chauffage au sol
Film isolation acoustique
Dalle béton 200mm
Couche ignifuge 80mm

R - 1 stationnement souterrain

Dalle béton 300mm
Isolation thermique rigide 300mm
Film pare vapeur
Gravier 200mm

Extérieur
Sable stabilisé
Argile expansée
Couche de filtration d'eau en gravier et cailloux
Film pare vapeur
Isolation thermique rigide 250mm
Dalle béton 300mm
Couche ignifuge 80mm
Intérieur

- 7 Dalle béton armé
200x200mm
- 8 Moucharabieh en pierre réemployé du site
300x200x180mm
- 9 Bac végétation à faible entretien
- 10 Poutre structurelle béton armé
200x200mm
- 11 Mur refend cage d'escalier béton armé
200mm

Coup détail - Fenêtre en saillie
1:20