


Floor Plans

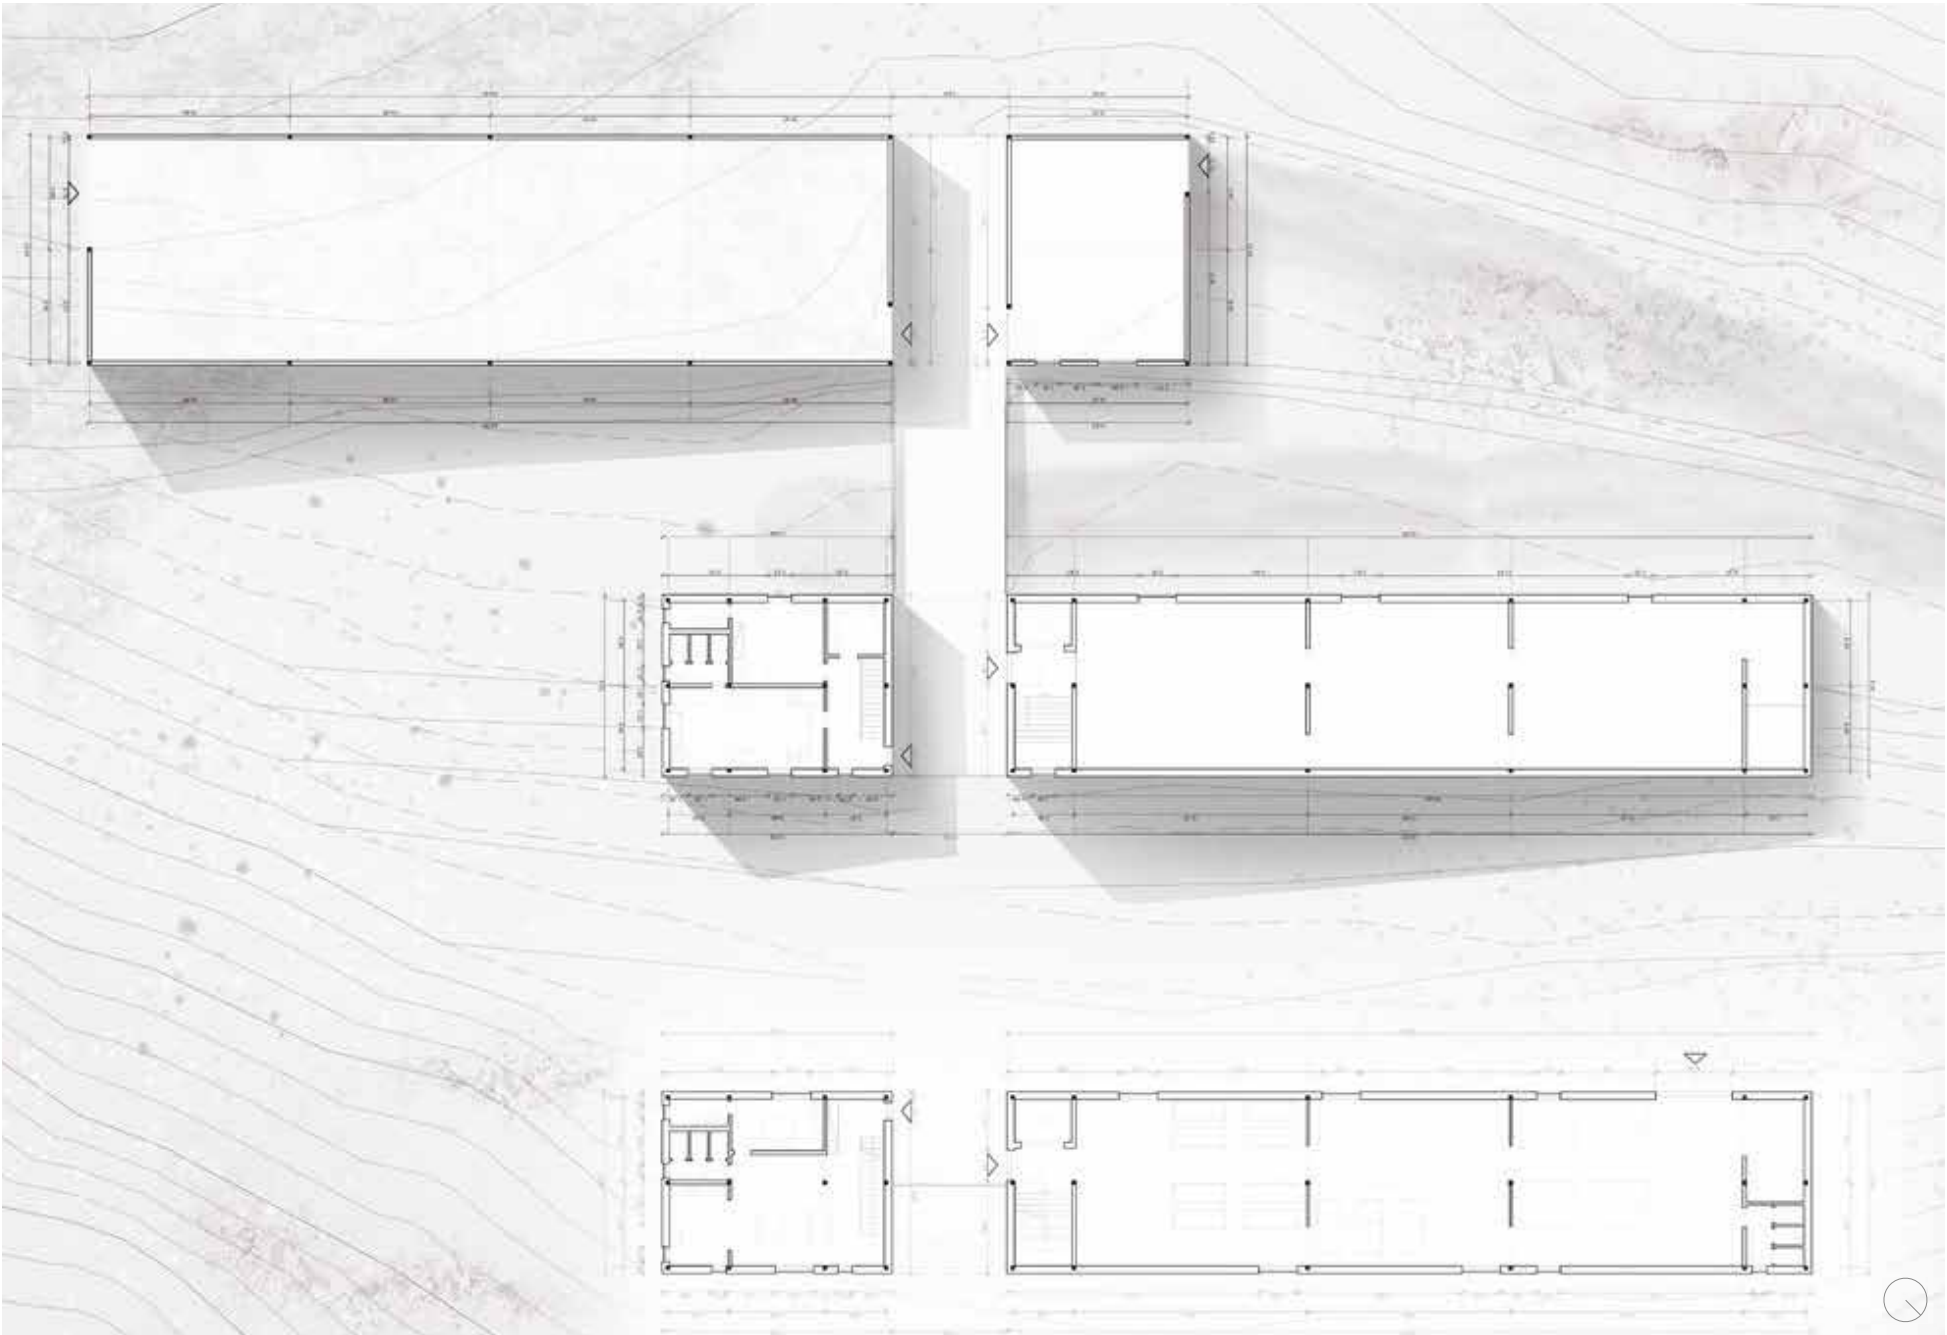

Perspective view of model

