



Floor Plans

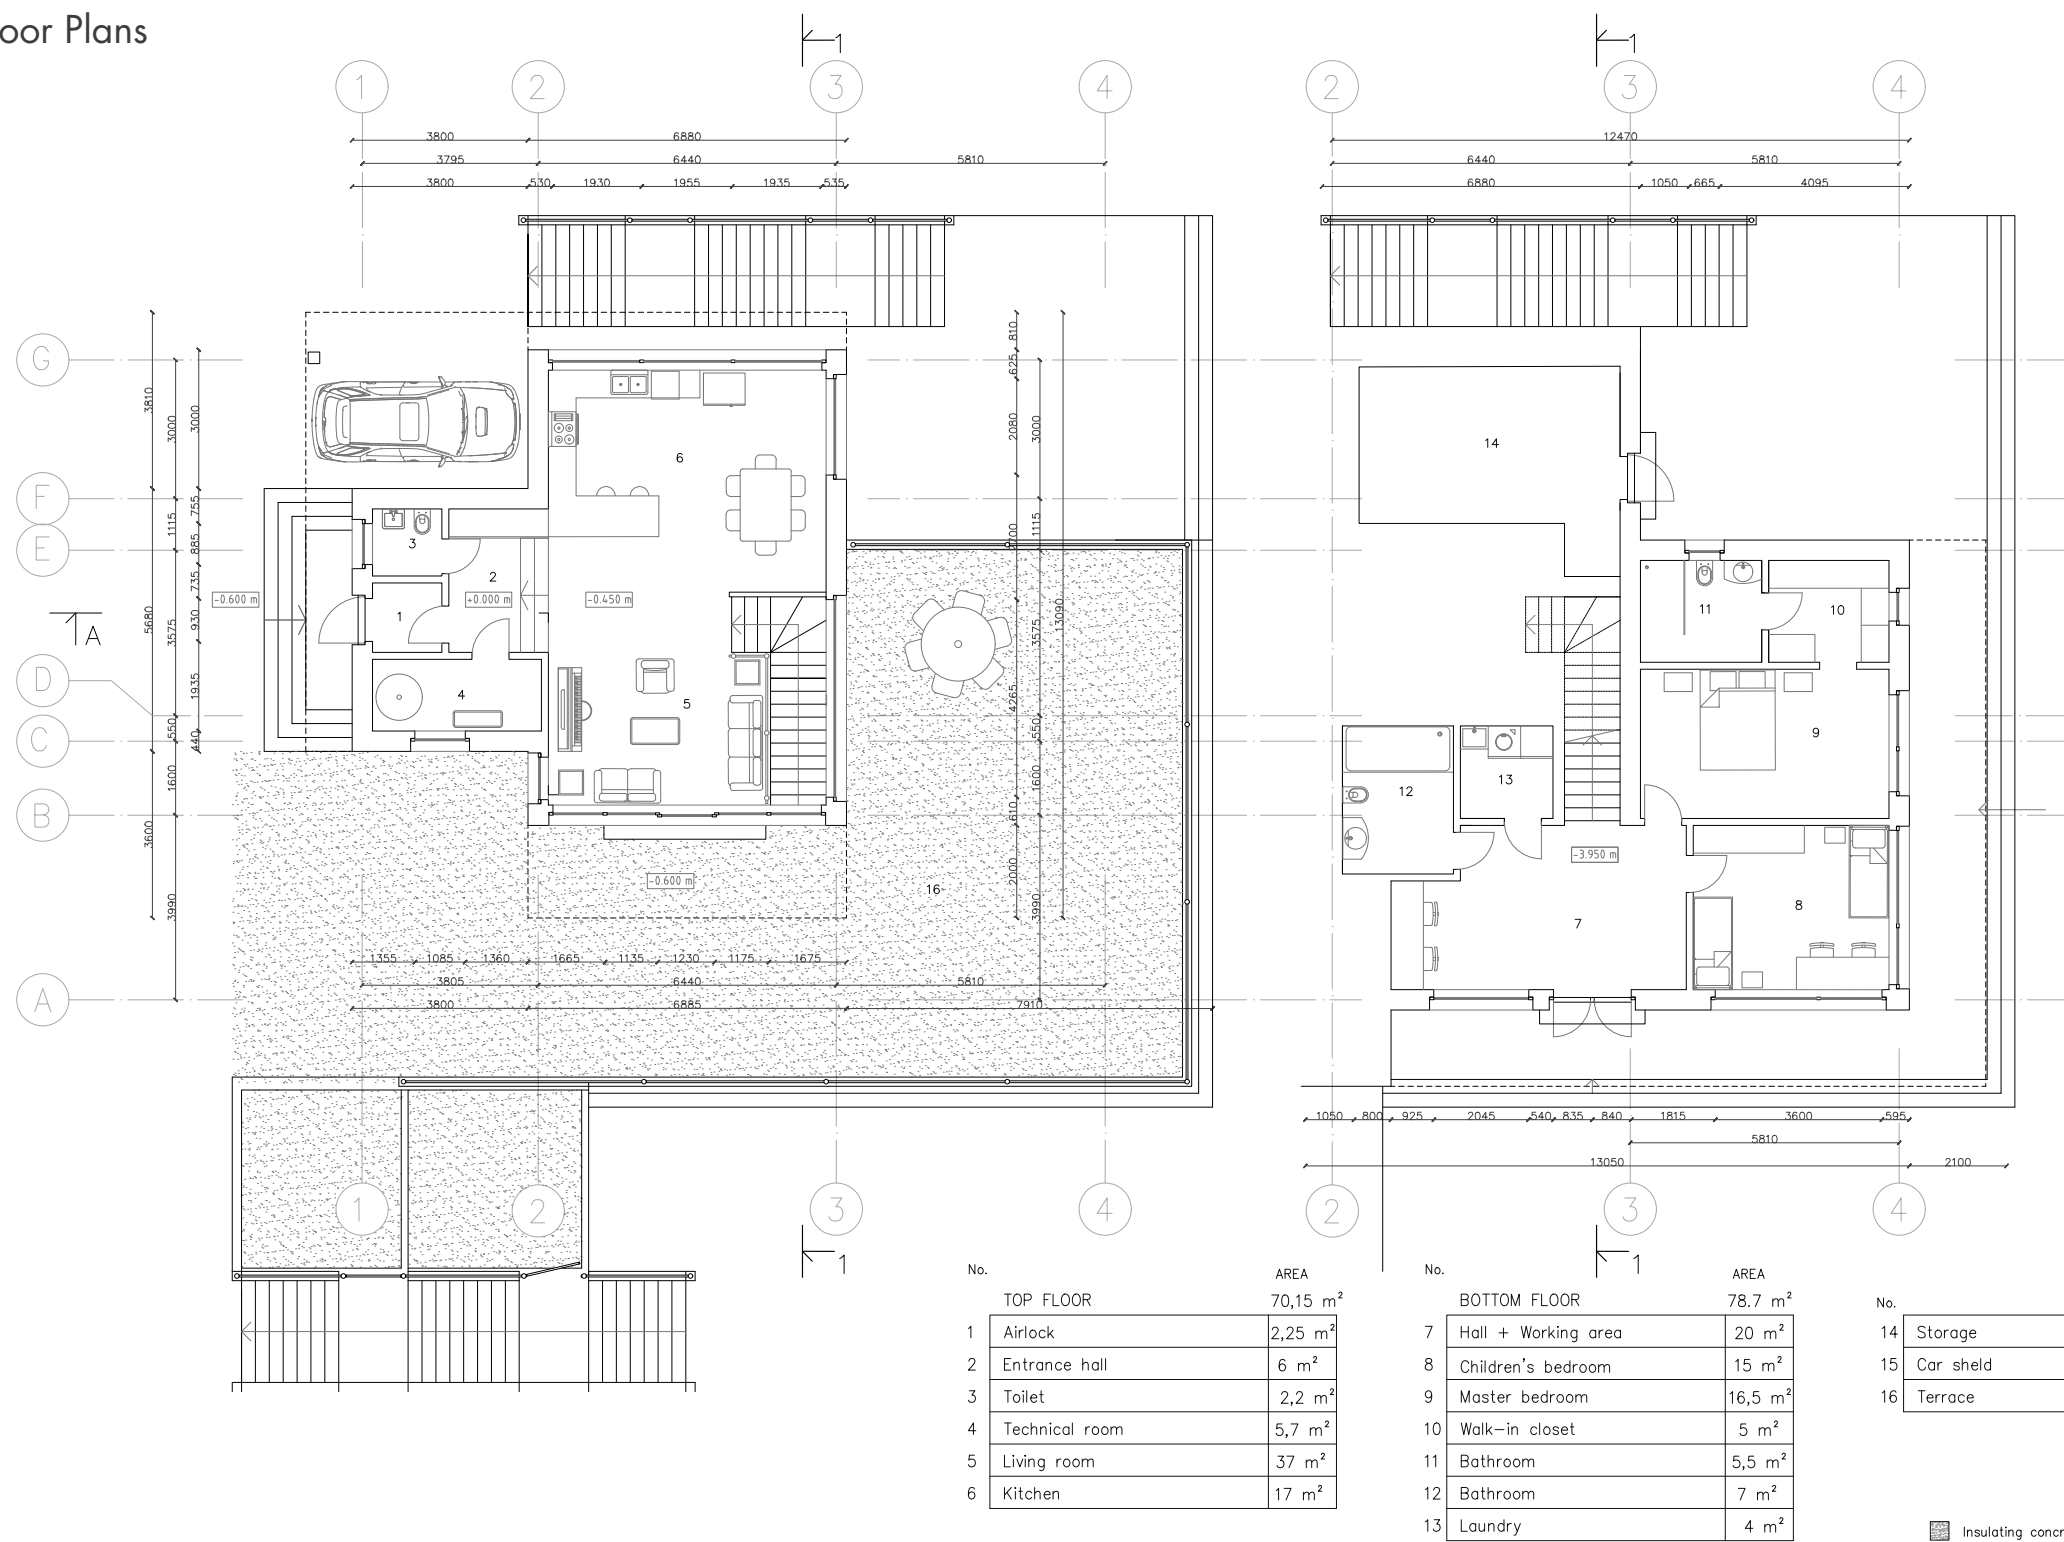

Sections

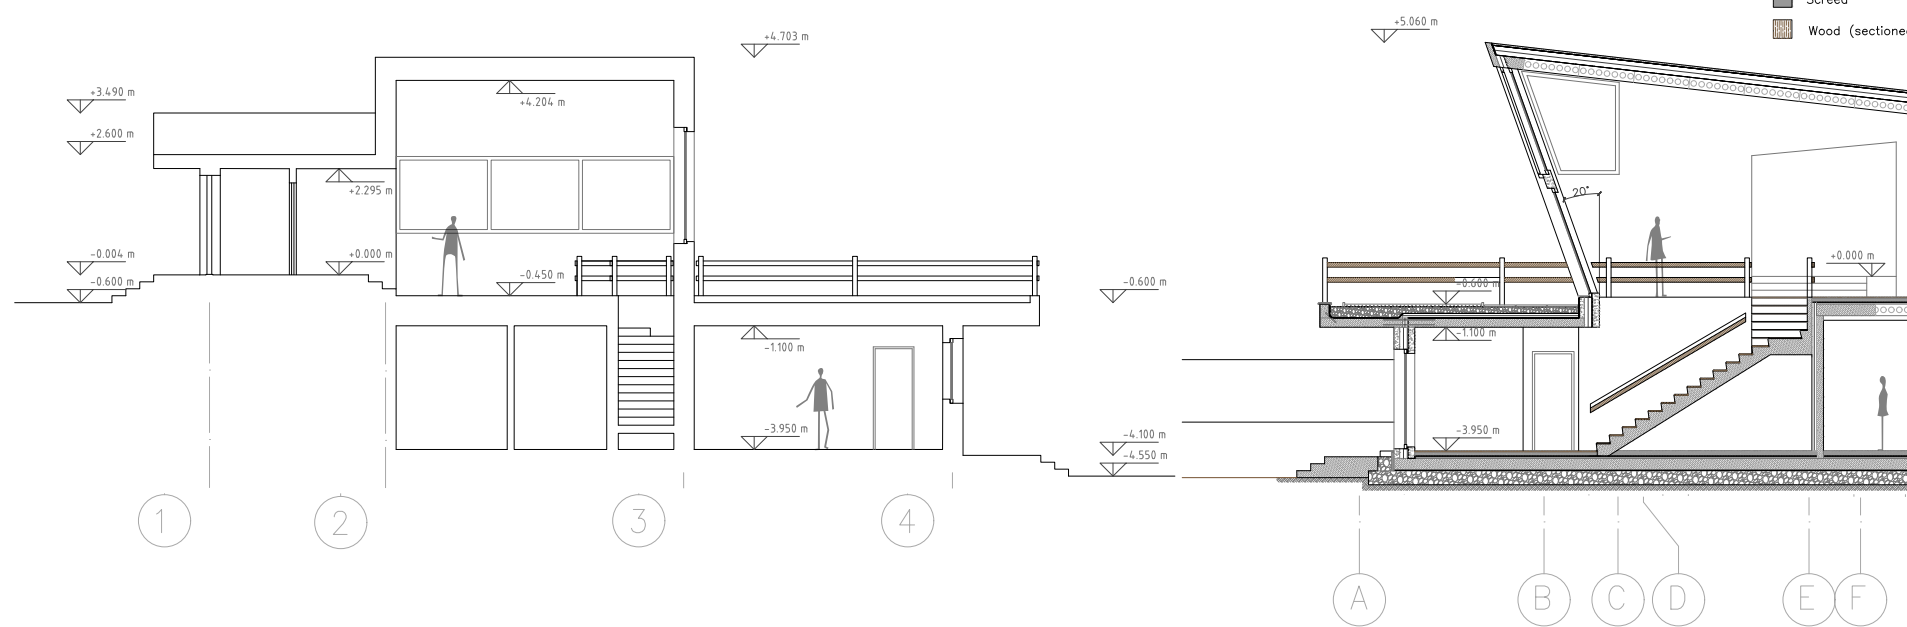

Façades

